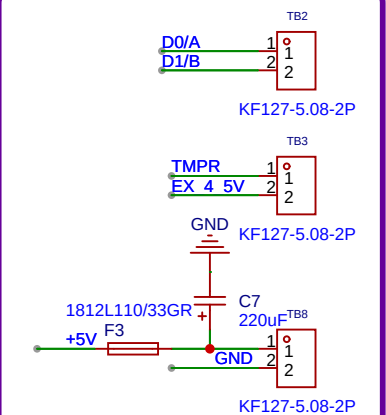
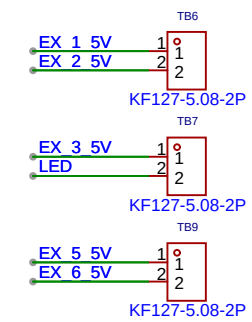
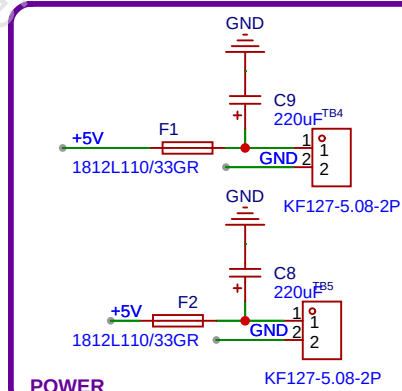
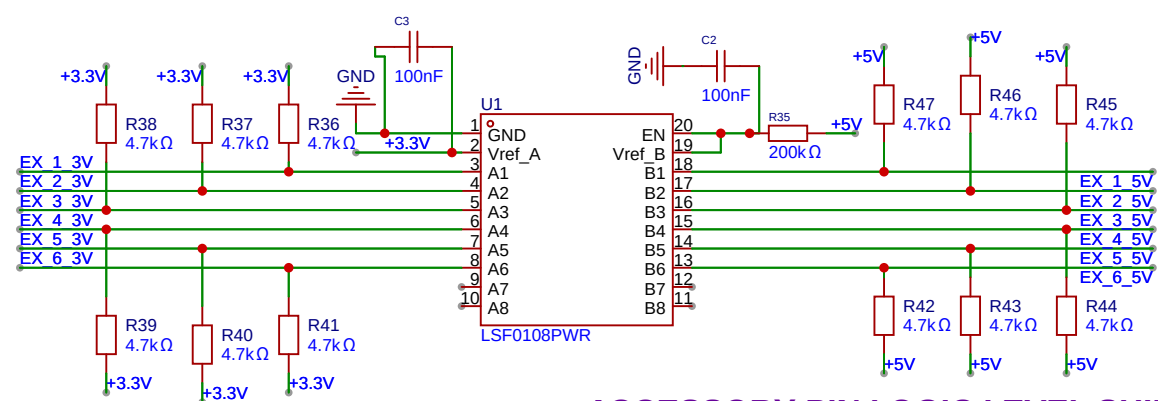
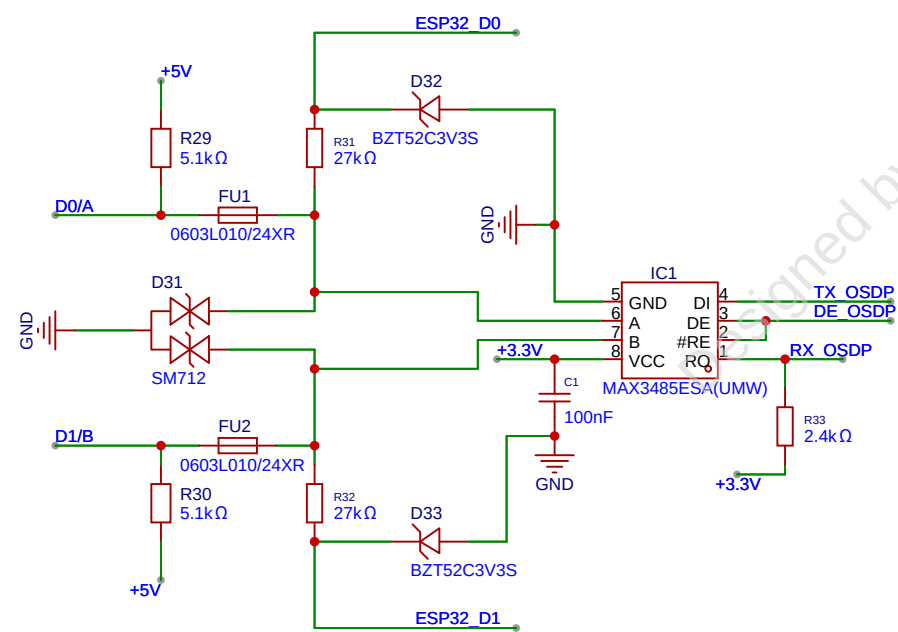
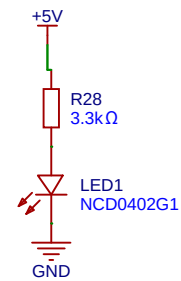
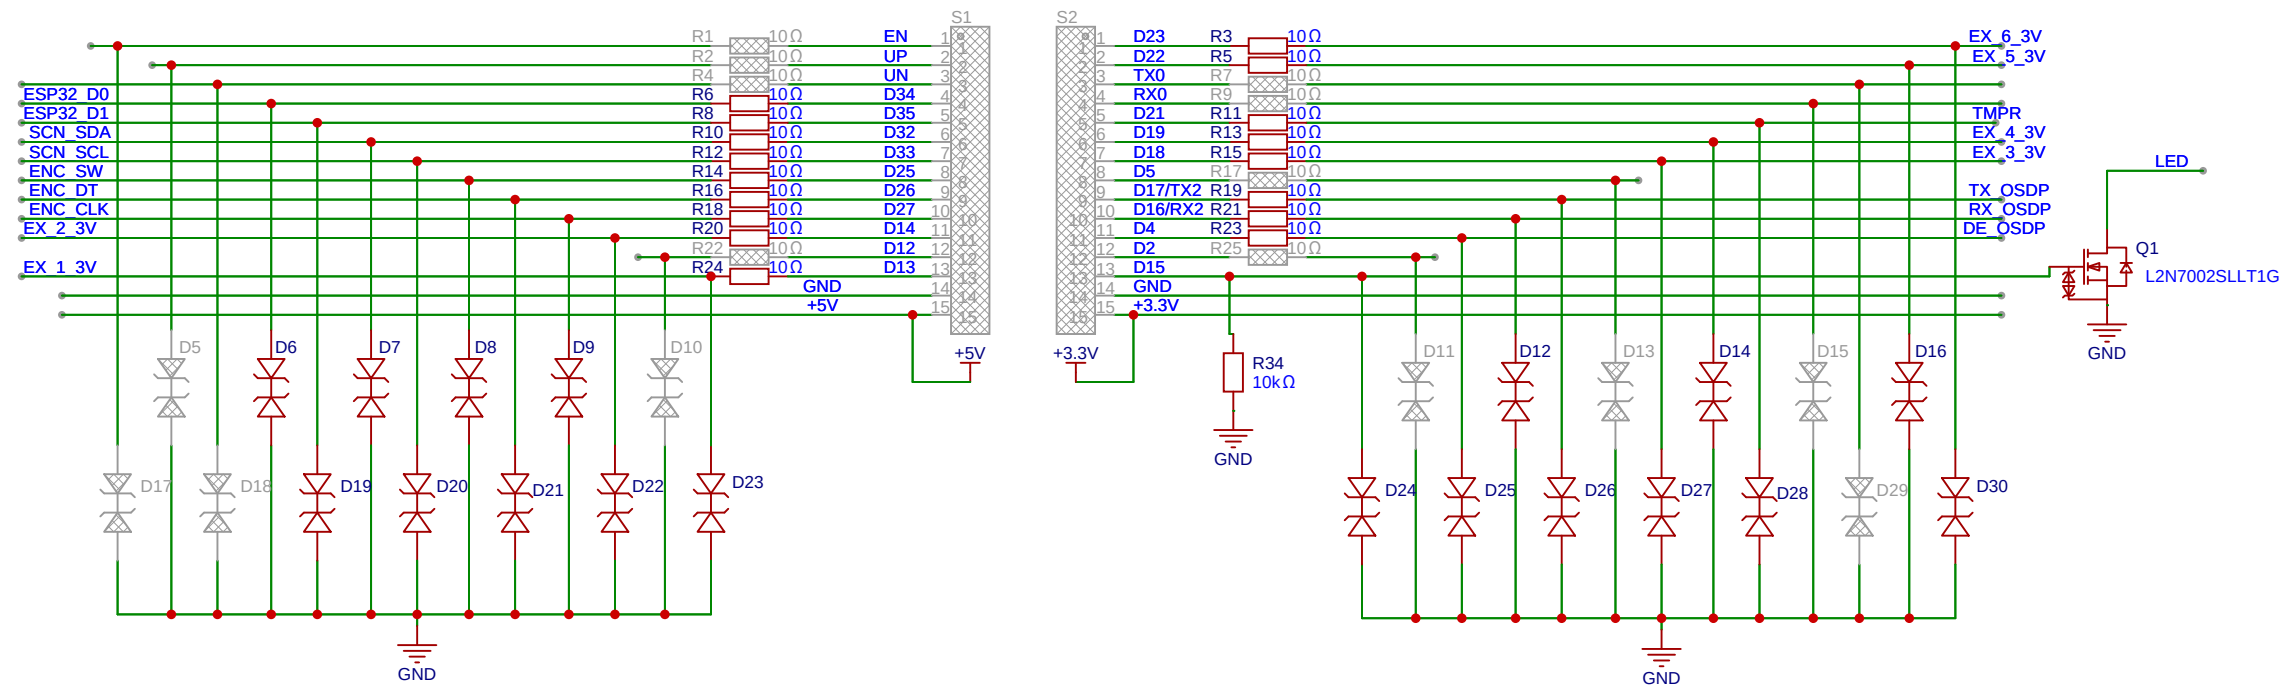


TERMINAL BLOCKS / THROUGH HOLES

Schematic	opendoorsim+			Create at	2026-04-21
				Update at	2026-05-20
Board	Board1			Page	P1
Drawn	Evan C	OpenDoorSim_ODSP			
Reviewed					
		Version	Size	Page 1 Total 1	
		V1.0		shortrange.tech	